

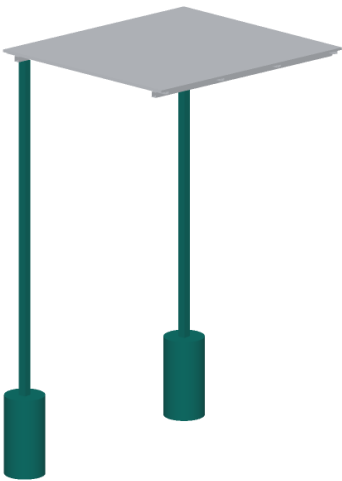


REV	DESCRIPTION	DATE	BY
P1	Making sketch for the prototype build plan	2026-10-03	AC

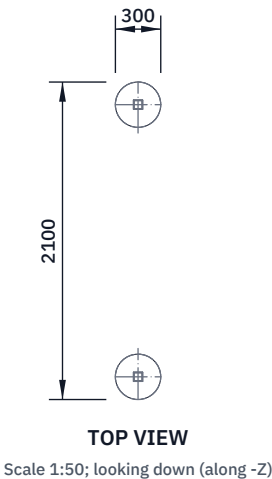

WHERE IT GOES
This part in colour, its neighbours in grey

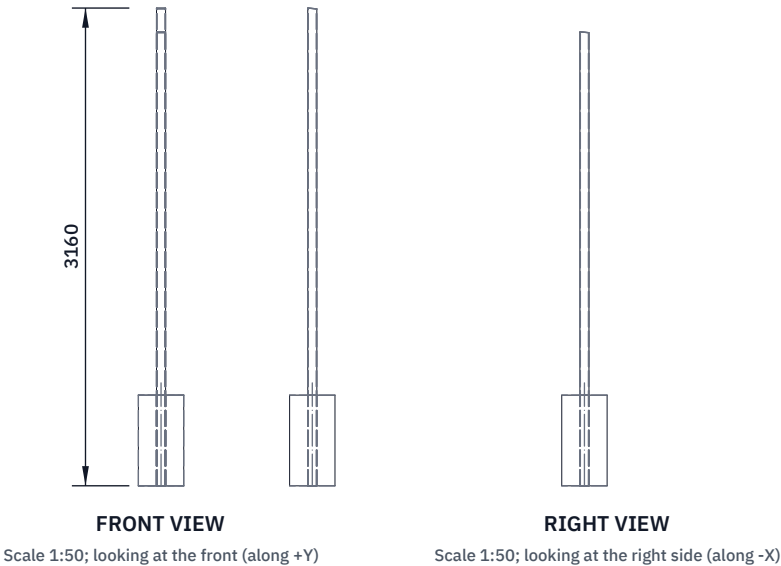

HOW TO MAKE IT AND HOW IT FITS

Four posts: two front (3,160 long) and two back (3,000 long), each set 600 into the ground; the tops are cut at 5 deg so the roof falls to the back. Back posts stand 2,400 above the ground.

Layout: 1,300 between post centres across, 1,800 front to back.

Holes: two 13 mm holes across each post top, 60 down, for the beam cleats; 9 mm holes for the box, siren and sign brackets on site.

Paint the buried 700 mm with bitumen; cap the tops.

Collars: auger 300 mm holes 650 deep; 50 mm of gravel; stand the post plumb on it and pour concrete to ground level, sloped to shed water.

Check: posts plumb within 5 mm over 2 m; diagonals equal within 10.

CAMPBREAK		github.com/BoujeeEnjinia1701/campbreak		
CampBreak station posts and concrete collars (left pair drawn): making sketch				
DRAWING NO. CBK-DWG-109		REV P1	SHEET 1 of 1	SIZE ANSI B
SCALE 1:50	UNITS mm	PROJECTION 	DATE 2026-10-03	DRAWN Amish Chadha
MATERIAL / NOTES 60 x 60 x 3 mm square tube, S235; concrete collars 300 mm across				
Licensed CERN-OHL-S-2.0 · Design Molecule Lab · designmolecule.com			Generated from cad/src; do not edit by hand	