


REV	DESCRIPTION	DATE	BY
P1	Making sketch for the prototype build plan	2026-10-03	AC

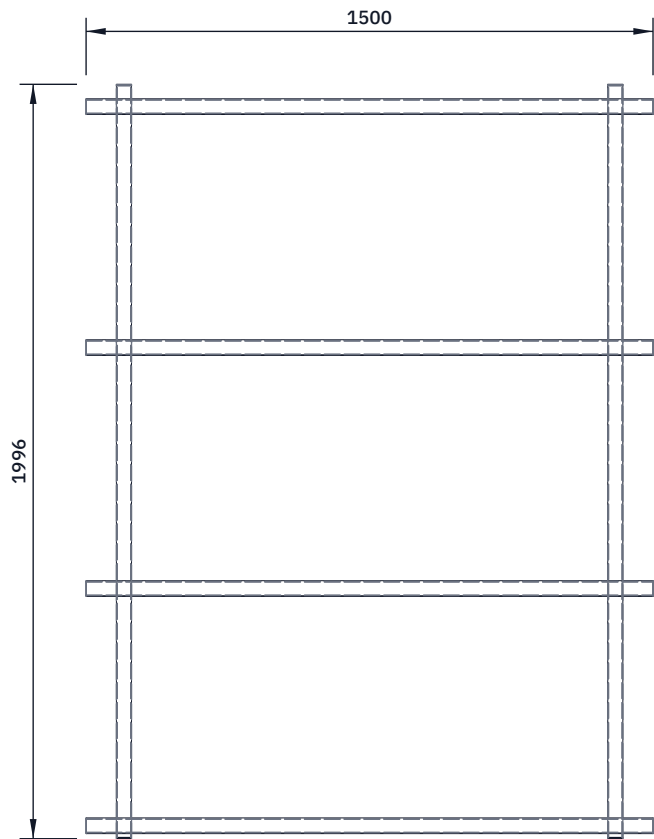

TOP VIEW

Scale 1:20; looking down (along -Z)




FRONT VIEW

Scale 1:20; looking at the front (along +Y)



RIGHT VIEW

Scale 1:20; looking at the right side (along -X)

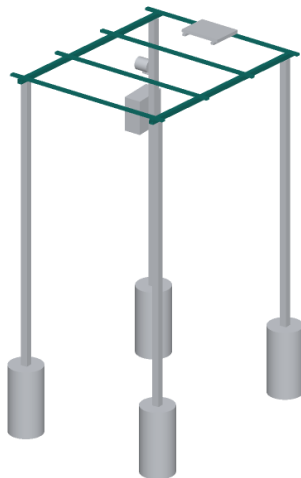

WHERE IT GOES

This part in colour, its neighbours in grey

HOW TO MAKE IT AND HOW IT FITS

Beams: two 40 x 40 x 2 tubes 2,000 long, one over each pair of posts, reaching 100 past the front and the back post centres.

Fix each beam to its post tops with a 40 x 40 x 4 angle cleat and two M8 bolts, or weld it on site.

Purlins: four 40 x 20 x 2 tubes 1,500 long across the beams, at 30, 660, 1,300 and 1,940 from the beams' front ends; weld or bolt with an M8 bolt through each crossing.

Roof sheet: corrugated galvanised 1,500 x 2,050, fixed to each purlin with roofing screws and washers on every second crest.

Check: the roof falls 5 deg to the back; no sheet edge overhangs a path by more than 100.

CAMPBREAK

github.com/BoujeeEnjinia1701/campbreak

CampBreak roof beams and purlins: making sketch

DRAWING NO. CBK-DWG-110			REV P1	SHEET 1 of 1	SIZE ANSI B
SCALE 1:20	UNITS mm	PROJECTION 	DATE 2026-10-03		DRAWN Amish Chadha
MATERIAL / NOTES 40 x 40 x 2 and 40 x 20 x 2 mm tube; S235					
Licensed CERN-OHL-S-2.0 · Design Molecule Lab · designmolecule.com				Generated from cad/src; do not edit by hand	